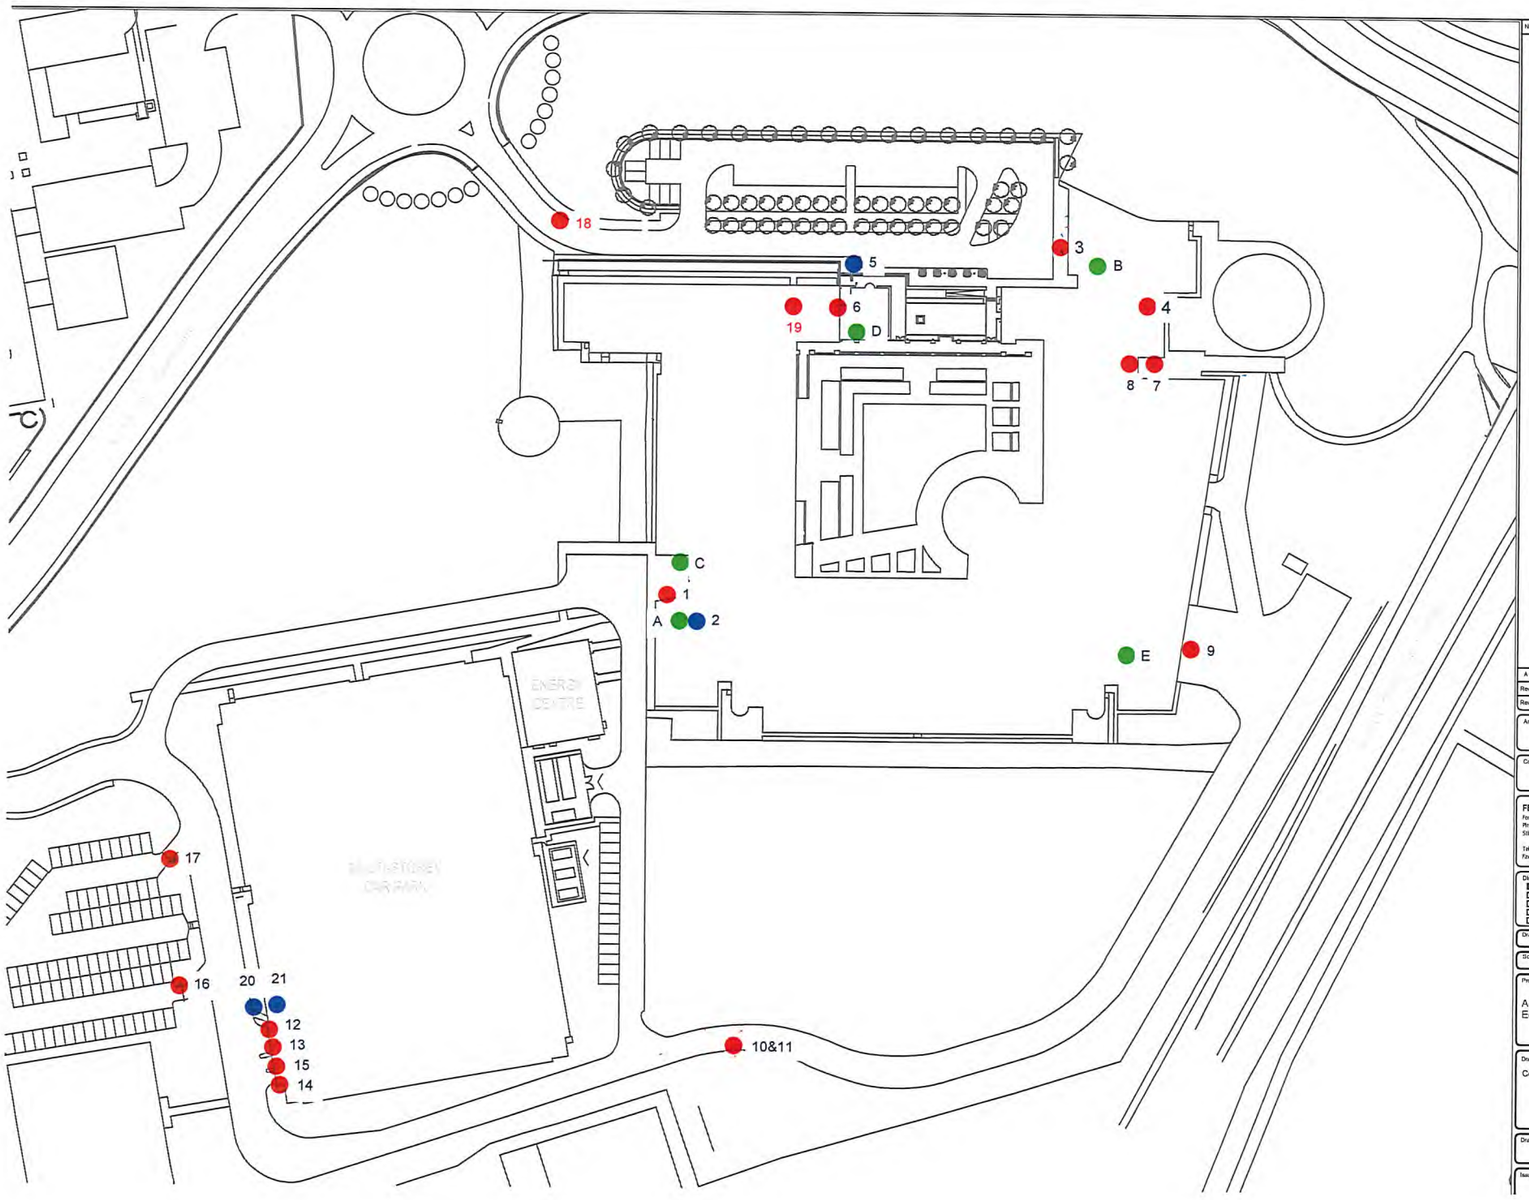

Notes

Audio & Video Intercom

Audio Intercom

Desktop Station

Rev d - MSCP cycle gate intercoms added

Rev	Description of Revision	Date
A	Camera positions moved, Lorry intercom moved	27/03/2013

Revision History

Architects Base Negative ID

Consultants Base Negative ID

FES Ltd.
Forth House
Pinnfield Business Park
Stirling, FK7 8HW
Tel. 01786 819 600
Fax. 01786 811 455

Discipline
- ■ Electrical Services
- ☐ Mechanical Services
- ☐ High Voltage Services
- ☐ Communications Services
- ☐ Fire Protection

Drawn: NM | Checked:

Scale: NTS | Date: 11/06/24

Project: Aegon Edinburgh Park

Drawing Title: Commend Intercom System

Drawing Number: | Revision: C

Issue Status: | Sheet:

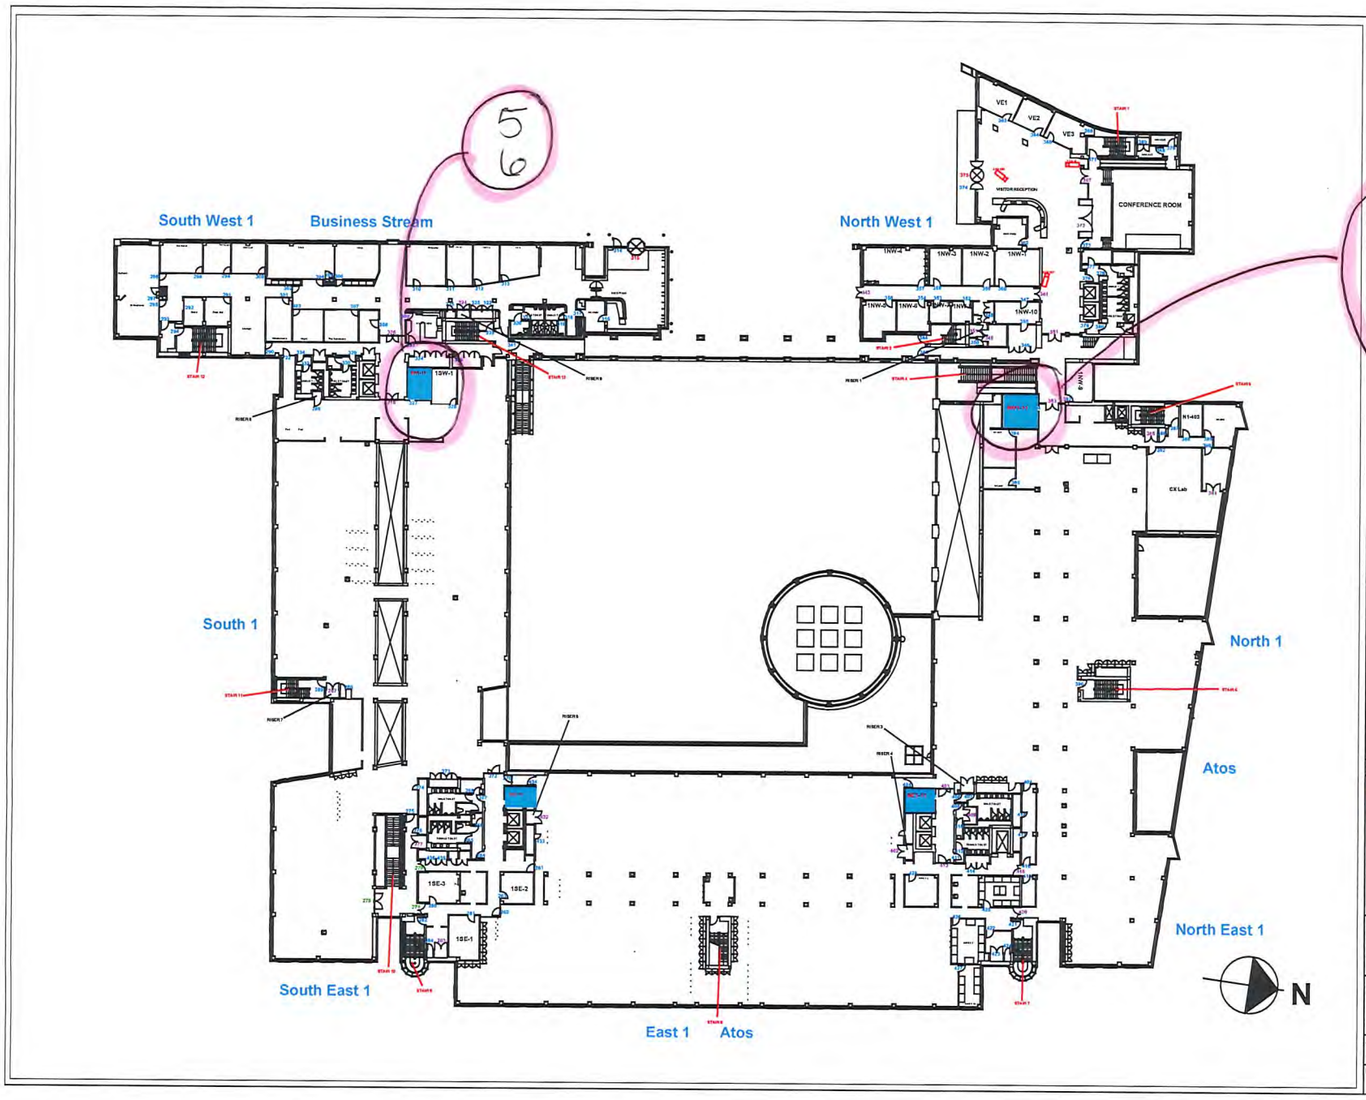

Doors Key :

Double Automatic Door

Double Manual Door

Single Manual Door

Revolving Manual Door

No.	Date	Revision

Notes & References

Filename:

aegon

Property Department
AEGON UK
Edinburgh Park
Edinburgh, EH12 9SE
Telephone: 0131-549 2222 www.aegon.co.uk
PropertyHelpdesk@aegon.co.uk

Location:
FIRST FLOOR
AEGON LOCHSIDE CRESCENT

Drawing Title:
CCTV CAMERAS

Scale @ A3:	Drawn By:	Date:
N.T.S.	L. Mahmoud	11/11/2024
Drawing No:		Revision:

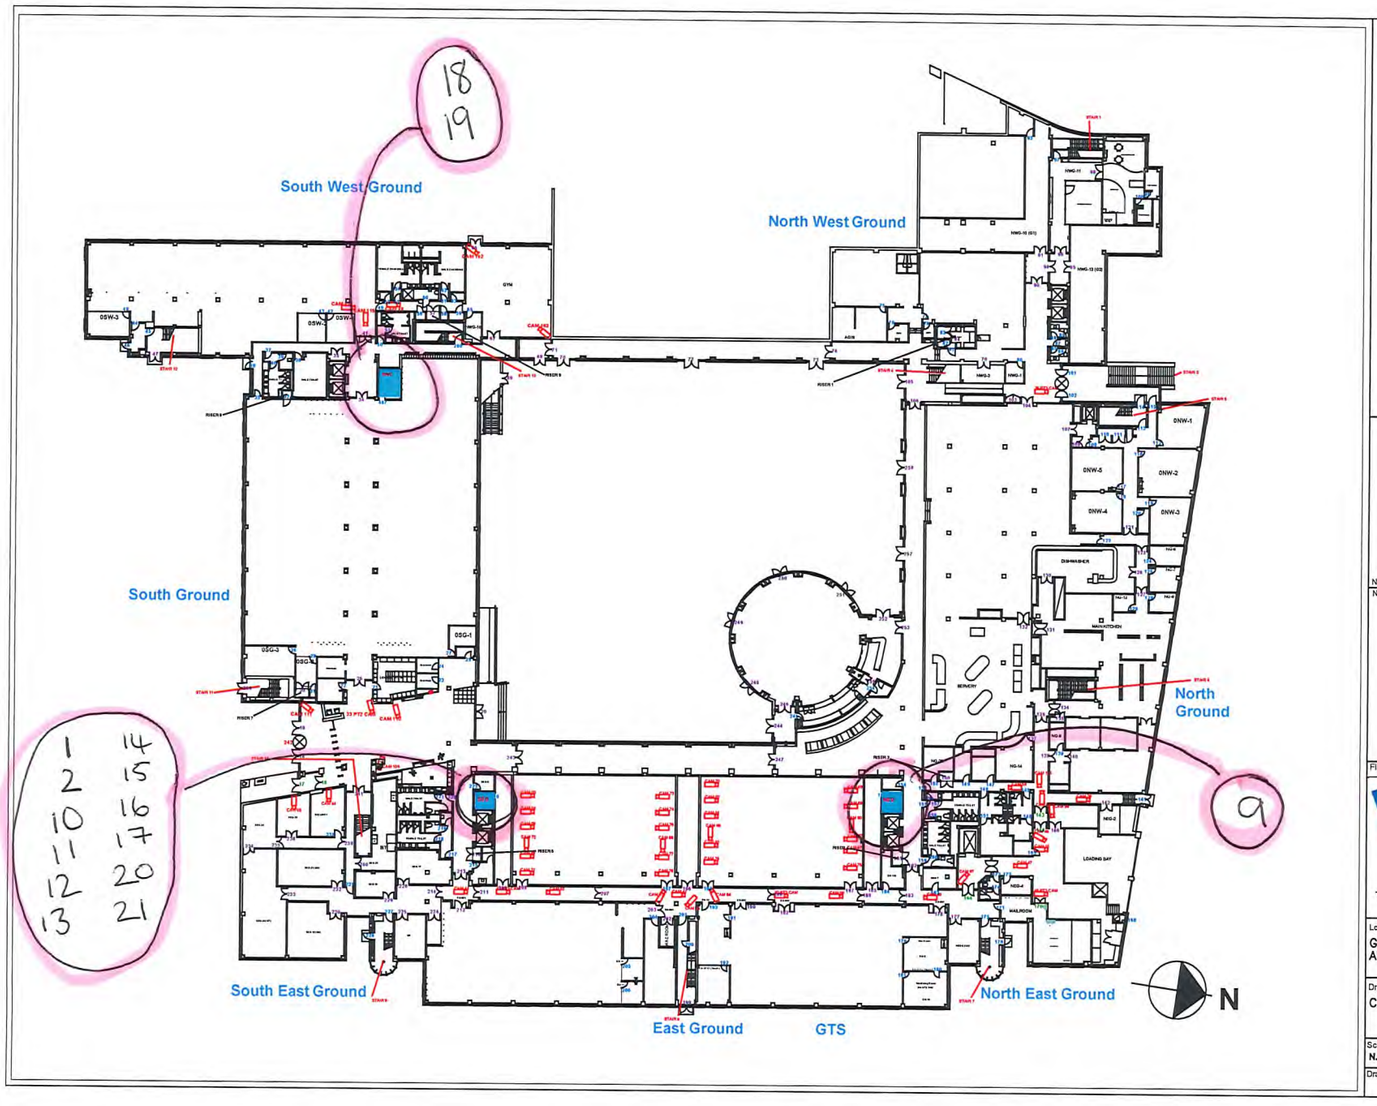

No.	Date	Revision

Notes & References

Filename:

aegon

Property Department
AEGON UK
Edinburgh Park
Edinburgh, EH12 9SE
Telephone: 0131-549 2222 www.aegon.co.uk
PropertyHelpdesk@aegon.co.uk

Location:
GROUND FLOOR
AEGON LOCHSIDE CRESCENT

Drawing Title:
CCTV CAMERAS

Scale @ A3:	Drawn By:	Date:
N.T.S.	L. Mahmoud	11/11/2024

Drawing No: | Revision:

AEGON, Edinburgh - Commend System

Rev d - Revised 12/07/24

	Call Point				Links To							
	Location	Floor	Audio	Video	Security Control Centre (A)	Staff Entrance desk (B)	Visitors Reception desk (C)	Business Stream desk (D)	Loading Bay (E)	Comments	SER Room	
1	Staff Entrance	Gnd	✓	✓		✓				after 30seconds (?) diverts to Security Control Centre	SEG	
2	Security Control Centre enrtrance door	Gnd	✓		✓						SEG	
3	Main Visitors Entrance - In	1st	✓	✓			✓			after 30seconds (?) diverts to Security Control Centre	NW1 or 2	
4	Main Visitors Entrance - Out	1st	✓	✓			✓			after 30seconds (?) diverts to Security Control Centre	NW1	
5	Business Stream - In	1st	✓					✓		after 30seconds (?) diverts to Security Control Centre	SW1	
6	Business Stream - Out	1st	✓	✓				✓		after 30seconds (?) diverts to Security Control Centre	SW1	
7	North Entrance - In	Gnd	✓	✓	✓						NW1	
8	North Entrance - Out	Gnd	✓	✓	✓						NW1	
9	Loading Bay	Gnd	✓	✓					✓	after 30seconds (?) diverts to Security Control Centre	NEG	
10	Service Road barrier - upper call point	Ext	✓	✓	✓						SEG	
11	Service Road barrier - lower call point	Ext	✓	✓	✓						SEG	
12	MSCP - In LHS	Ext	✓	✓	✓						SEG	
13	MSCP - In RHS	Ext	✓	✓	✓						SEG	
14	MSCP - Out LHS	Ext	✓	✓	✓						SEG	
15	MSCP - Out RHS	Ext	✓	✓	✓						SEG	
16	Over Flow Carpark - In	Ext	✓	✓	✓						SEG	
17	Over Flow Carpark - Out	Ext	✓	✓	✓						SEG	
	Provision For											
18	Road into Visitors Entrance	Ext	✓	✓							SWG	
19	Gymnasium/Fitness Suite	Gnd	✓	✓							SWG	
20	MSCP Cycle Gate - In	Ext	✓		✓						SEG	added 12/07/24
21	MSCP Cycle Gate - Out	Ext	✓		✓						SEG	added 12/07/24